



FOUNDATION PLAN NOTES

- A VERIFY ALL DIMENSIONS WITH THE ARCHITECTURAL DRAWINGS.
- B DETAILS ON THESE PLANS ARE INTENDED TO DEPICT THE GENERAL CONSTRUCTION METHODS FOR THIS STRUCTURE. CONNECTIONS, DETAILS AND CONDITIONS NOT SPECIFICALLY SHOWN THAT ARE SIMILAR TO THOSE THAT ARE SPECIFIED SHALL BE ASSUMED ONE AND THE SAME. IF QUESTIONS REGARDING THE APPLICATION OF DETAILS ARE ENCOUNTERED, NOTIFY THE ARCHITECT / ENGINEER FOR CLARIFICATION IN A TIMELY MANNER PRIOR TO BID OPENING.
- C FOR A COMPLETE LIST OF CALLOUTS & SYMBOLS SEE SHEET S000.
- D FOR A COMPLETE LIST OF SCHEDULES SEE SHEET SXXX.
- E ALL FOOTINGS SHALL BEAR ON UNDISTURBED NATIVE SOILS OR ENGINEERED FILL PREPARED IN ACCORDANCE WITH THE RECOMMENDATIONS IN THE PROJECT GEOTECHNICAL REPORT.
- F SUBGRADE REQUIREMENTS, UNDERSLAB VAPOR BARRIER AND PERIMETER FOUNDATION DRAINAGE SHALL BE PROVIDED IN ACCORDANCE WITH THE RECOMMENDATIONS IN THE PROJECT GEOTECHNICAL REPORT.
- G STEP FOOTINGS, WHERE REQUIRED, FROM ELEVATION TO ELEVATION IN ACCORDANCE DETAIL 5/S500.
- H THE CONTRACTOR IS TO LAYOUT CONCRETE SLAB CONTROL JOINTS PER THE CRITERIA IN THE "CONCRETE" SECTION OF THE GENERAL STRUCTURAL NOTES AND DETAIL XXXXX. THE CONTRACTOR MUST SUBMIT A CONTROL JOINT PLAN TO THE ARCHITECT AND STRUCTURAL ENGINEER OF RECORD FOR REVIEW AND APPROVAL AT LEAST (10) BUSINESS DAYS PRIOR TO SLAB POUR.
- I REFERENCE THE ARCHITECTURAL DRAWINGS FOR TOP OF SLAB ELEVATIONS AND LOCATIONS WHERE CHANGES IN SLAB ELEVATION OCCUR.
- J ANCHOR BOLTS AND PLATE WASHERS AT SHEAR WALLS SHALL BE PLACED IN ACCORDANCE WITH THE REQUIREMENTS INDICATED IN DETAIL XXXXX.
- K PLACE REINFORCING BARS AT CORNERS AND INTERSECTIONS FOR FOUNDATIONS. BARS AT CORNERS AND INTERSECTIONS SHALL BE EQUAL IN SIZE, NUMBER AND SPACING TO HORIZONTAL REINFORCING.

FOOTING SCHEDULE			
	SIZE	REINFORCING	NOTES
1	1'-6" WIDE x 12" DEEP x CONT	(2) #5 CONT LONGITUDINAL AND #4 TRANSVERSE @ 16" OC TOP & BOTTOM	
2	2'-0" WIDE x 18" DEEP x CONT	(4) #5 CONT LONGITUDINAL TOP AND BOTTOM. #5 TRANSVERSE @ 16" OC TOP & BOTTOM	
3	2'-6" WIDE x 18" DEEP x CONT	(5) #5 CONT LONGITUDINAL TOP AND BOTTOM. #5 TRANSVERSE @ 16" OC TOP & BOTTOM	
4	4'-0" x 4'-0" x 18"	(4) #6 EQ SPACED EACH DIRECTION AT BOTTOM	
5	6'-0" x 6'-0" x 18"	(6) #6 EQ SPACED EACH DIRECTION AT BOTTOM	

Structural Keyed Notes

- 2 4" CONCRETE SLAB-ON-GRADE WITH #3 BARS EACH WAY AT 16"OC.
- 3 FOOTING ON PROPERTY LINE SUPPORTED WITH CONCRETE PIERS OR MICROPILES.
- 6 SET FOOTINGS AT ELEVATION OF ELEVATOR FOUNDATION. STEP FOOTINGS DOWN PER 5/S500.



NOT FOR
CONSTRUCTION

50% DESIGN DEVELOPMENT

Issue Date: 05.22.2017

COPYRIGHT:
THESE PLANS ARE AN INSTRUMENT OF THE SERVICE AND ARE THE PROPERTY OF THE ARCHITECT, AND MAY NOT BE DUPLICATED, DISCLOSED, OR REPRODUCED WITHOUT THE WRITTEN CONSENT OF THE ARCHITECT. COPYRIGHTS AND INFRINGEMENTS WILL BE ENFORCED AND PROSECUTED.


REVISIONS:

FOUNDATION PLAN


Sheet Name

S200



Sheet Number

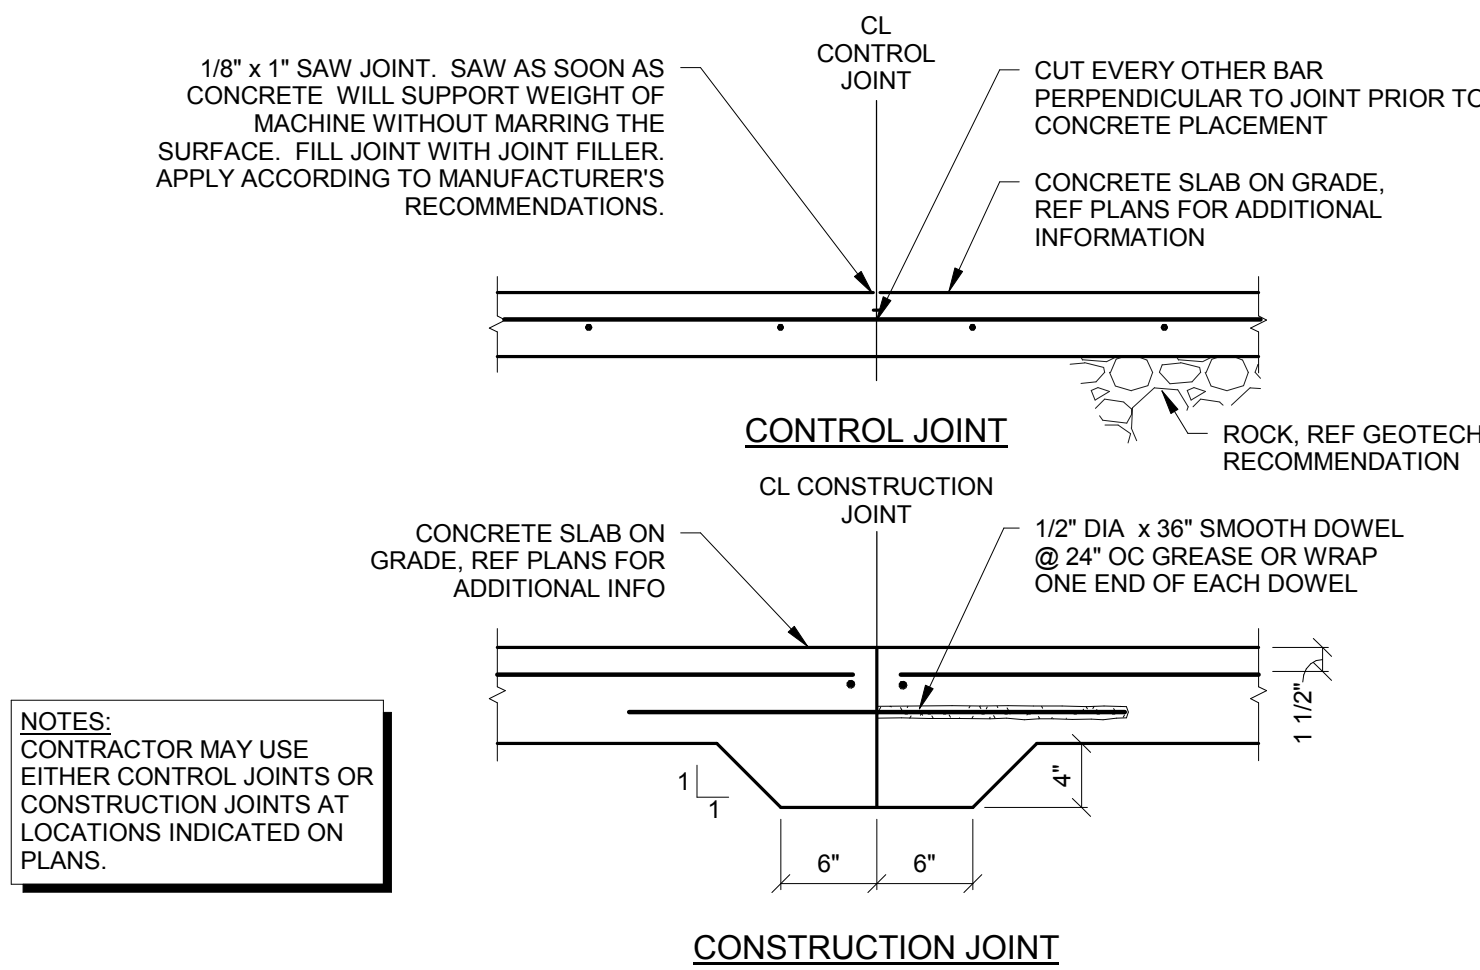


6
S500
SLAB JOINTS
1" = 1'-0"

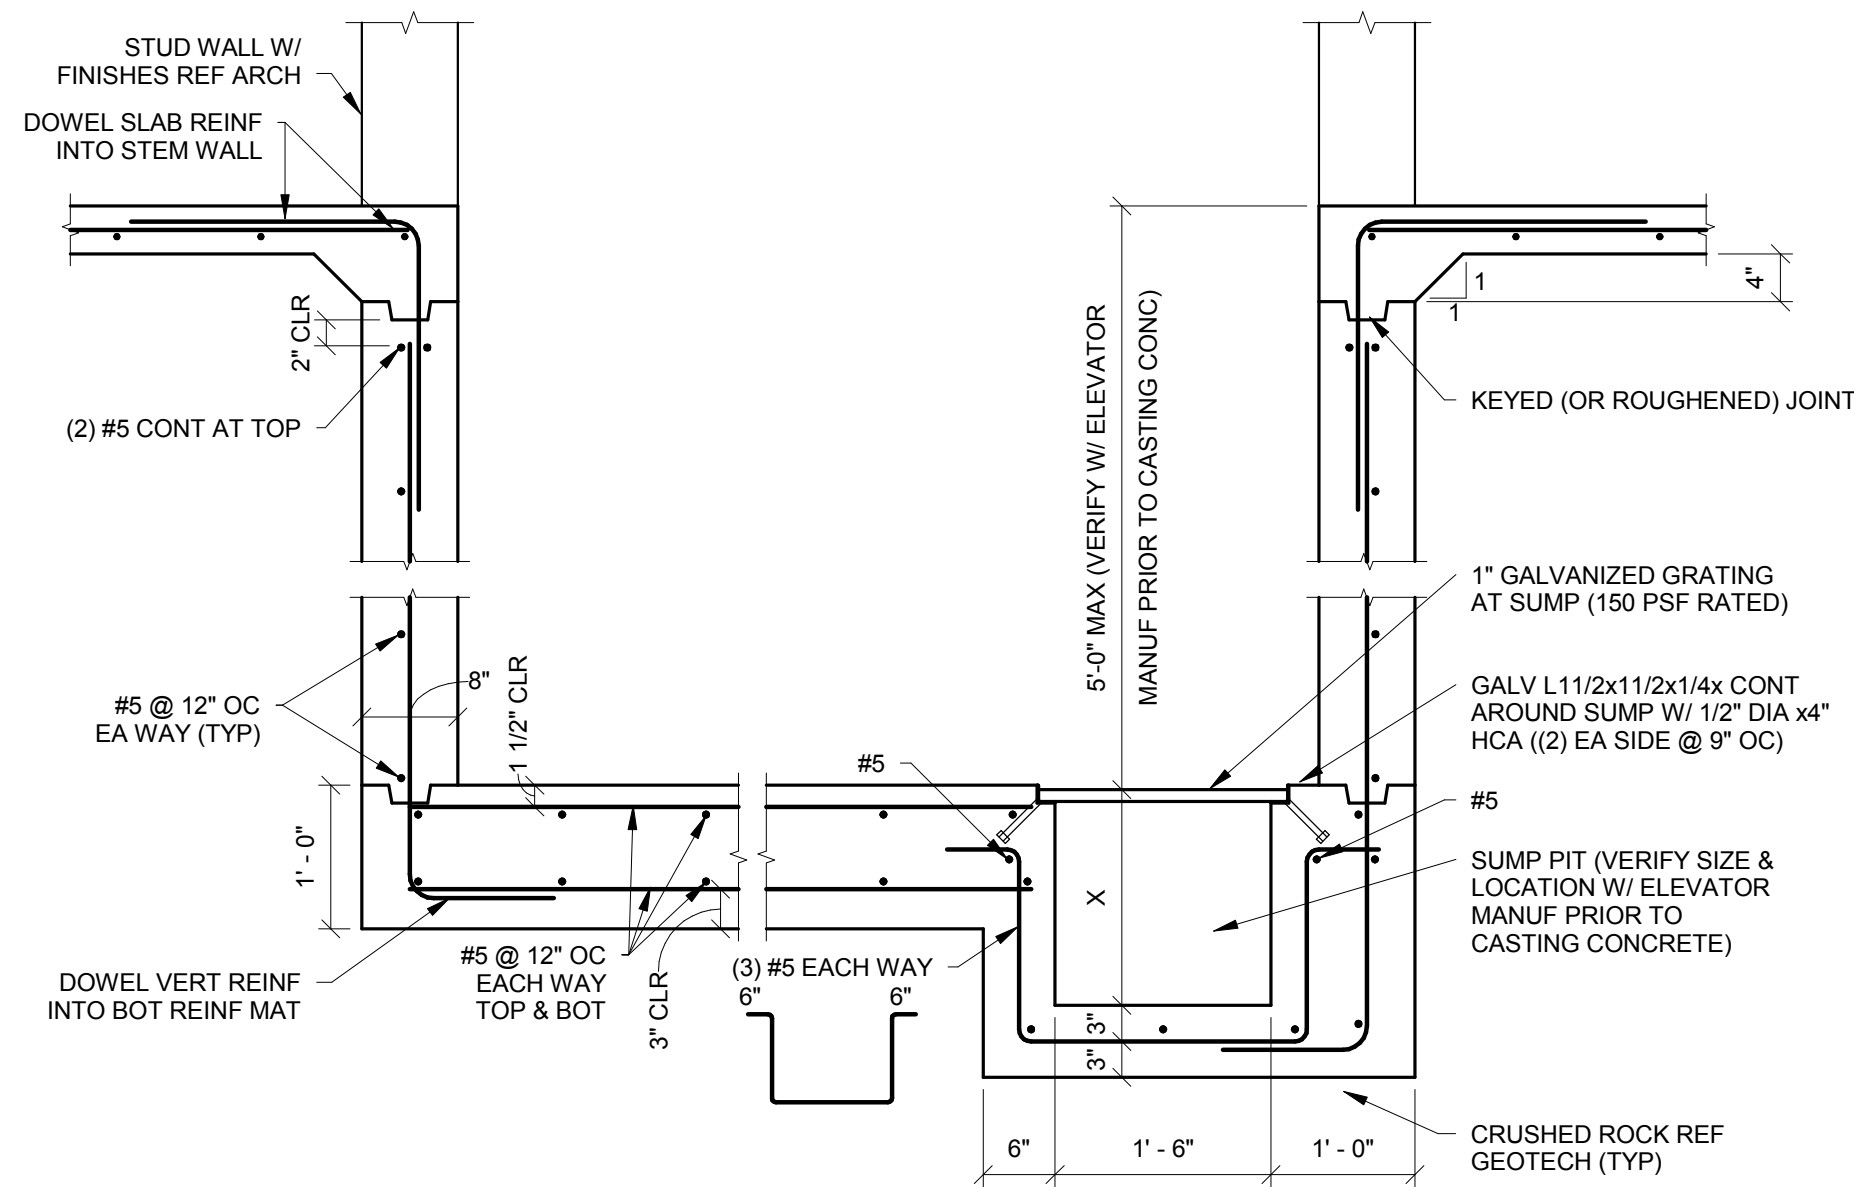


7
S500
ELEVATOR PIT - SECTION
3/4" = 1'-0"

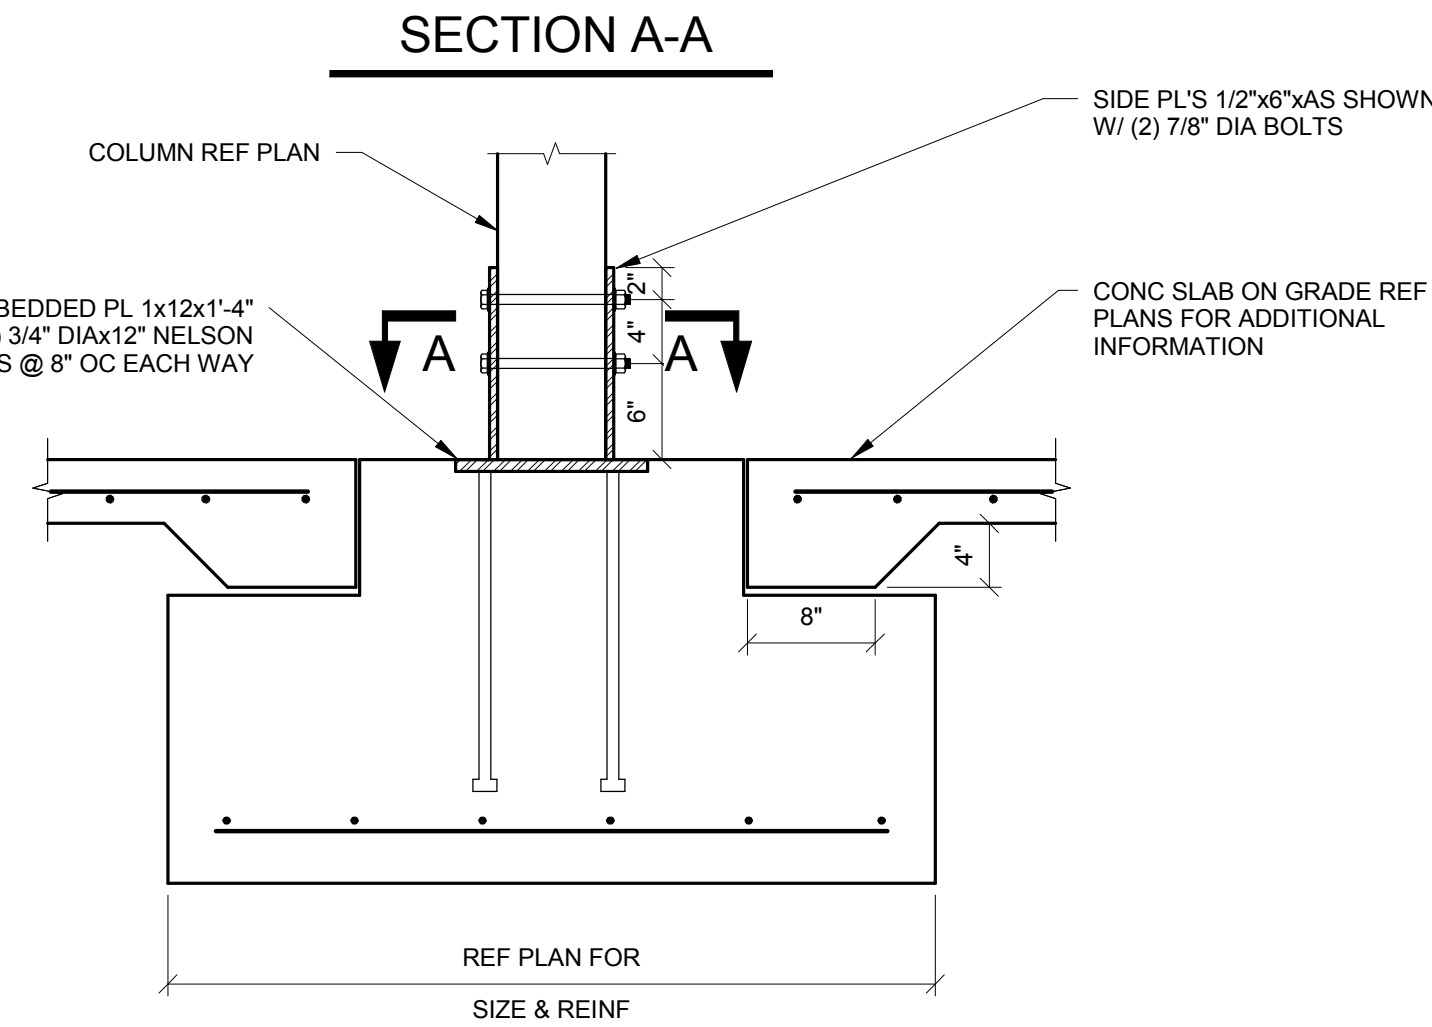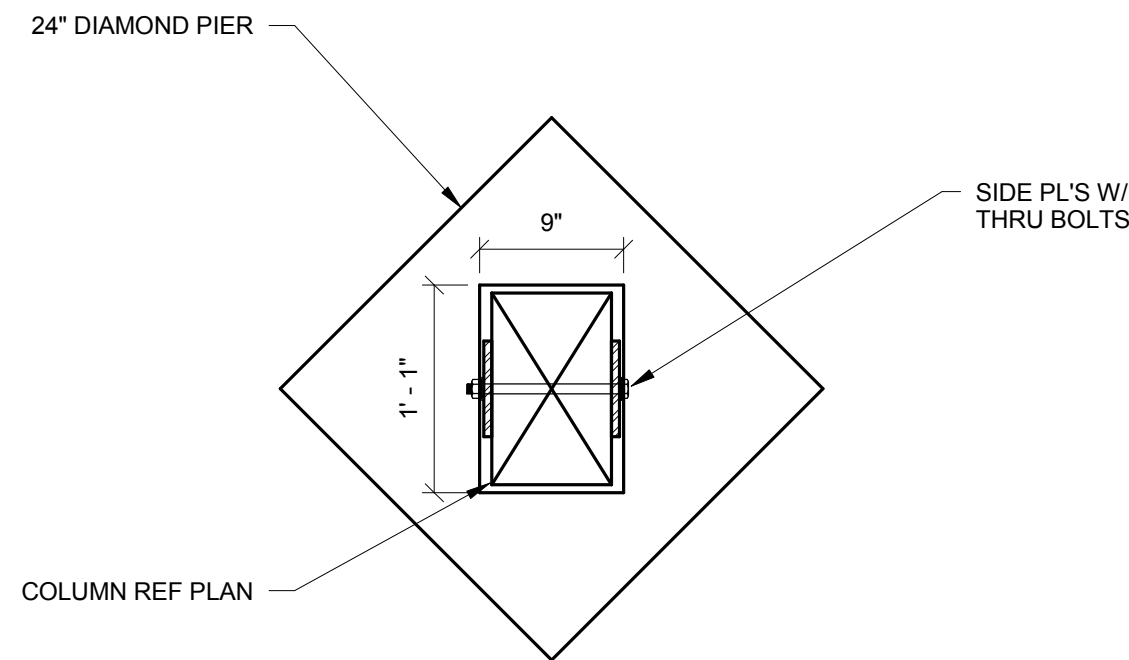

3
S500
GL COLUMN TO FOUNDATION
1" = 1'-0"

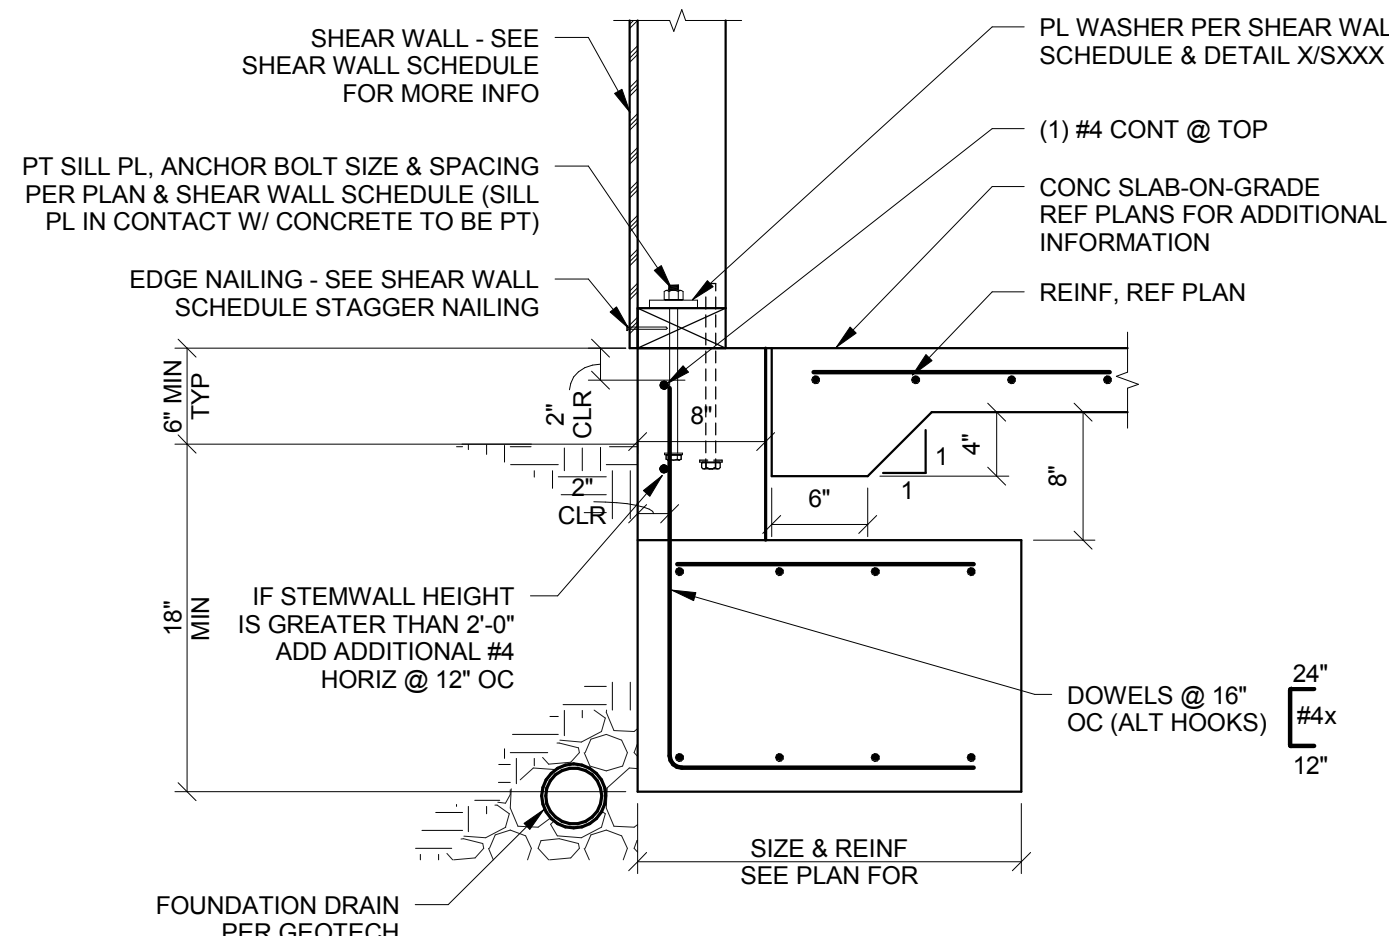


4
S500
EXTERIOR WALL AT FOUNDATION
1" = 1'-0"

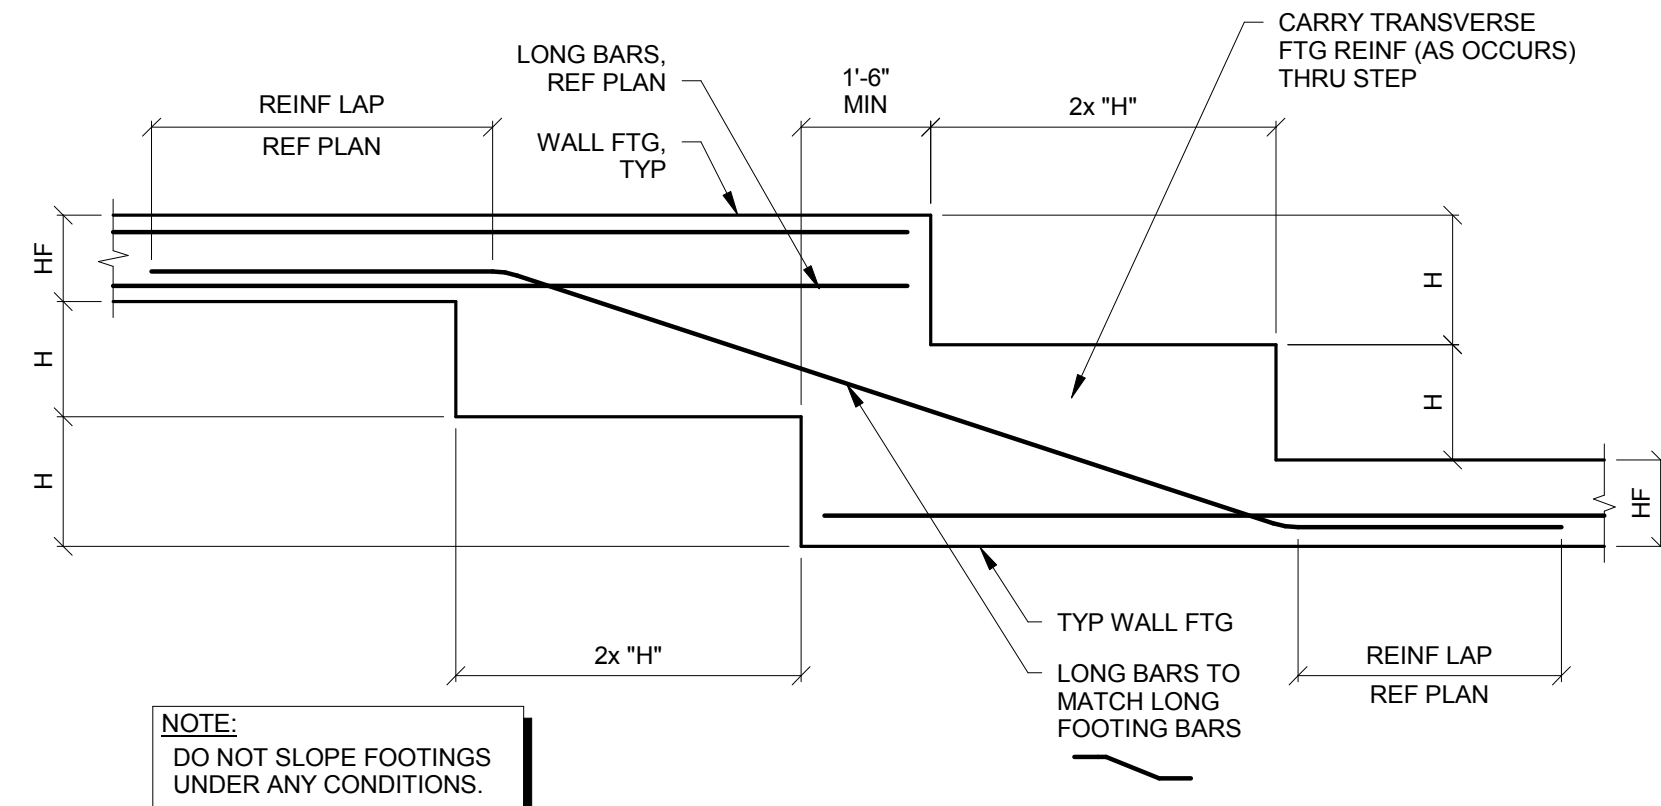


5
S500
STEPPED FOOTING
1" = 1'-0"

CONTRACTOR'S OPTION:
REPLACE CAST-IN-PLACE ANCHOR BOLT WITH EITHER:
1. 5/8" DIA WEDGE BOLT, EMBED 5" MINIMUM (SAMPSON STRONG-BOLT OR HILTI KWIK BOLT TX)
OR
2. 5/8" DIA A307 THREADED ROD, EPOXY EMBED 5" MINIMUM (SIMPSON SET-XP OR HILTI RE 500 SD)

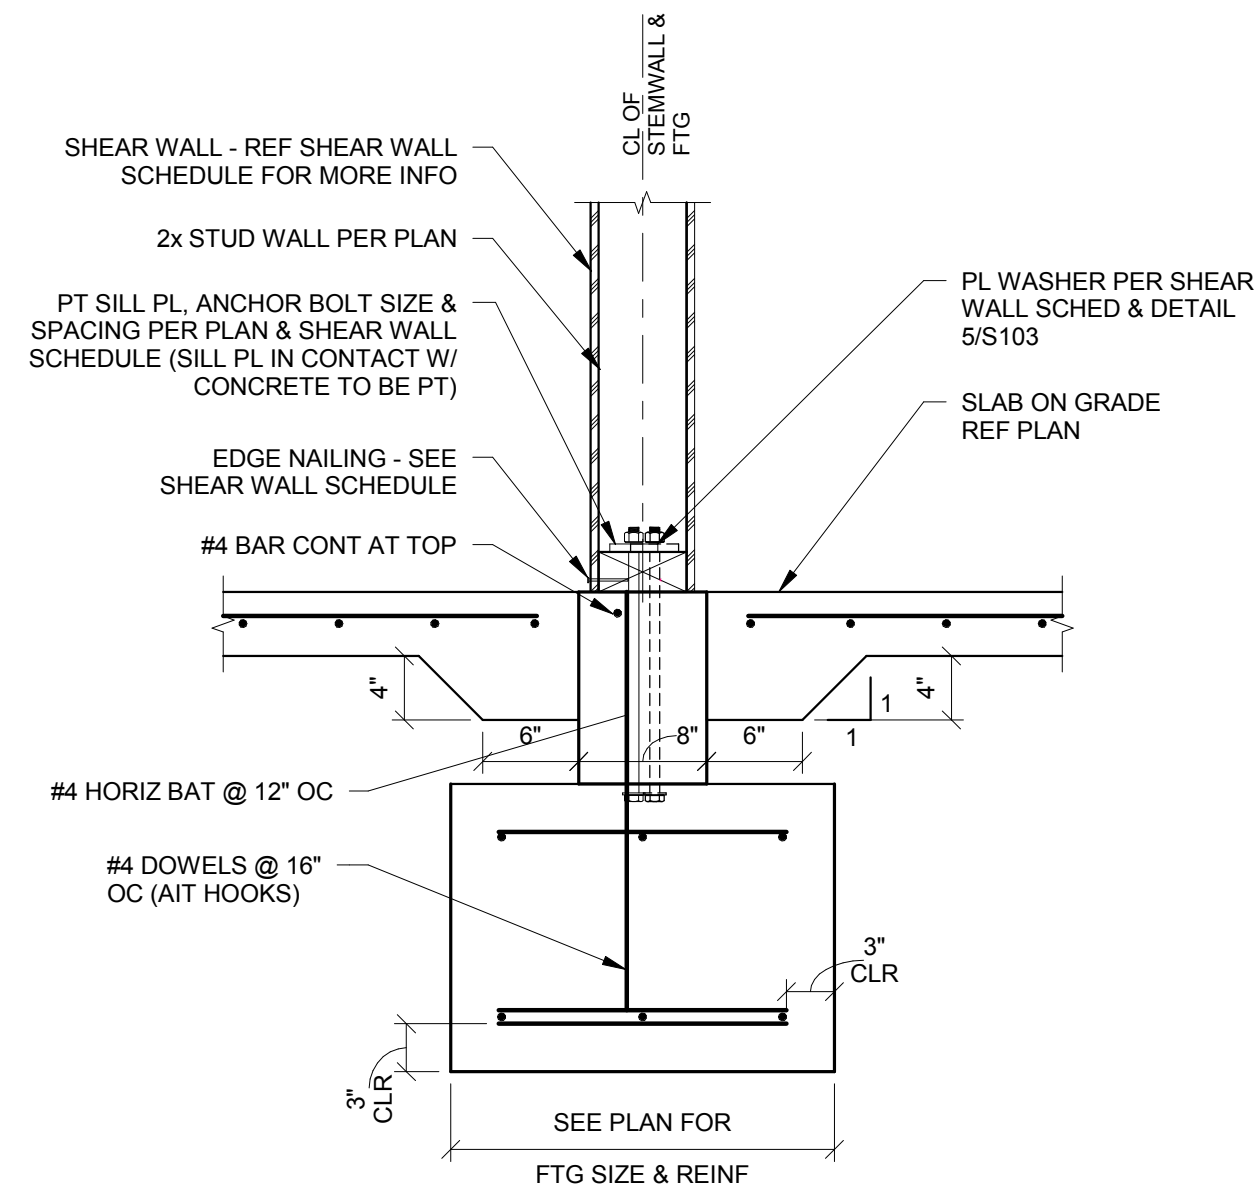

1
S500
INTERIOR SHEAR WALL TO THICKENED SLAB
1" = 1'-0"

CONTRACTOR'S OPTION:
REPLACE CAST-IN-PLACE ANCHOR BOLT WITH EITHER:
1. 5/8" DIA WEDGE BOLT, EMBED 5" MINIMUM (SAMPSON STRONG-BOLT OR HILTI KWIK BOLT TX)
OR
2. 5/8" DIA A307 THREADED ROD, EPOXY EMBED 5" MINIMUM (SIMPSON SET-XP OR HILTI RE 500 SD)

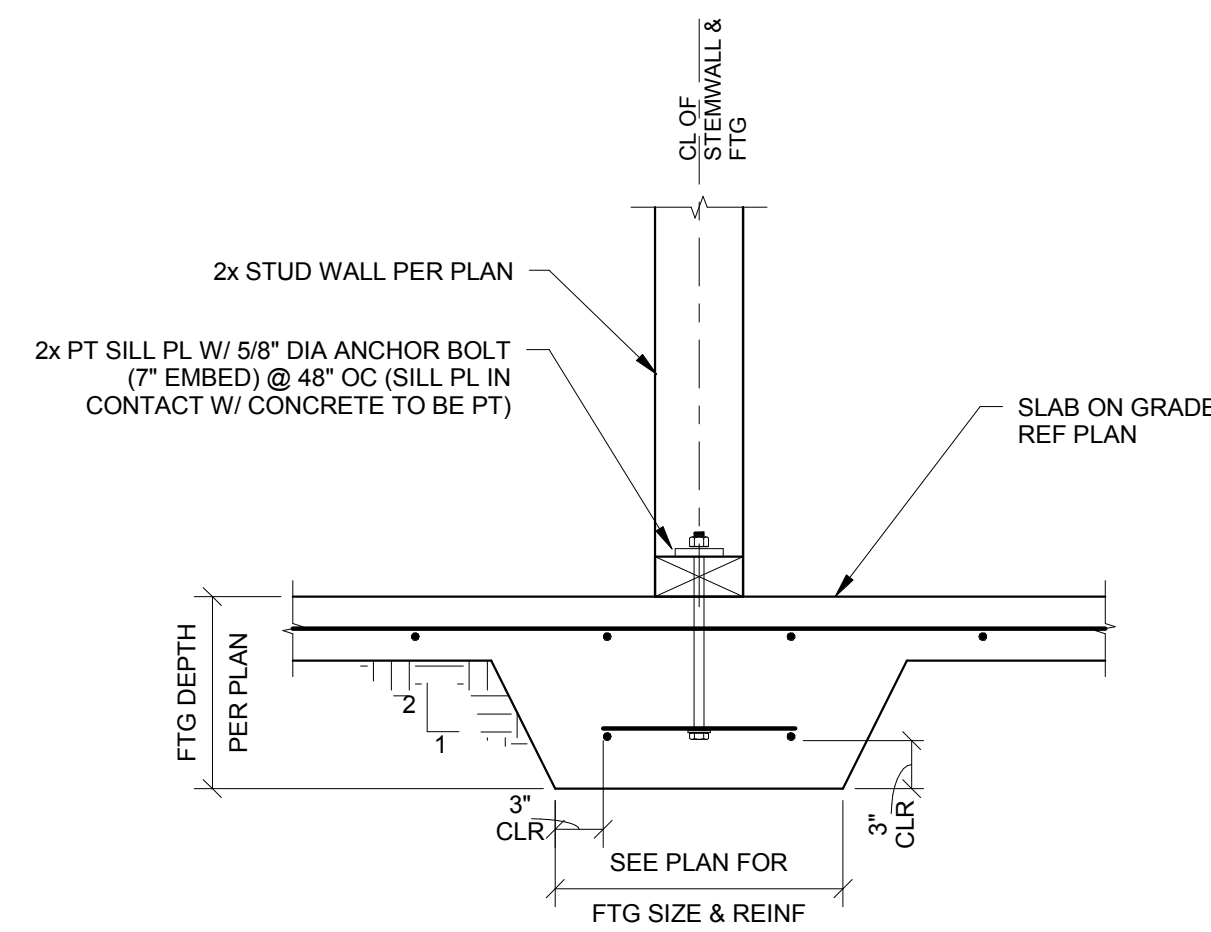

2
S500
INTERIOR SHEAR WALL TO THICKENED SLAB
1" = 1'-0"



NOT FOR
CONSTRUCTION

50% DESIGN DEVELOPMENT

Issue Date: 05.22.2017

COPYRIGHT:
THESE PLANS ARE AN INSTRUMENT OF THE SERVICE AND ARE THE PROPERTY OF THE ARCHITECT, AND MAY NOT BE DUPLICATED, DISCLOSED, OR REPRODUCED WITHOUT THE WRITTEN CONSENT OF THE ARCHITECT. COPYRIGHTS AND INFRINGEMENTS WILL BE ENFORCED AND PROSECUTED.

REVISIONS:

FOUNDATION DETAILS

Sheet Name

S500

Sheet Number